


XXXX-XX-XX-XX-XXXX-XXXX-XX-XXXX-XX

NOTAS DEL CONTRATISTA O SUBCONTRATISTA

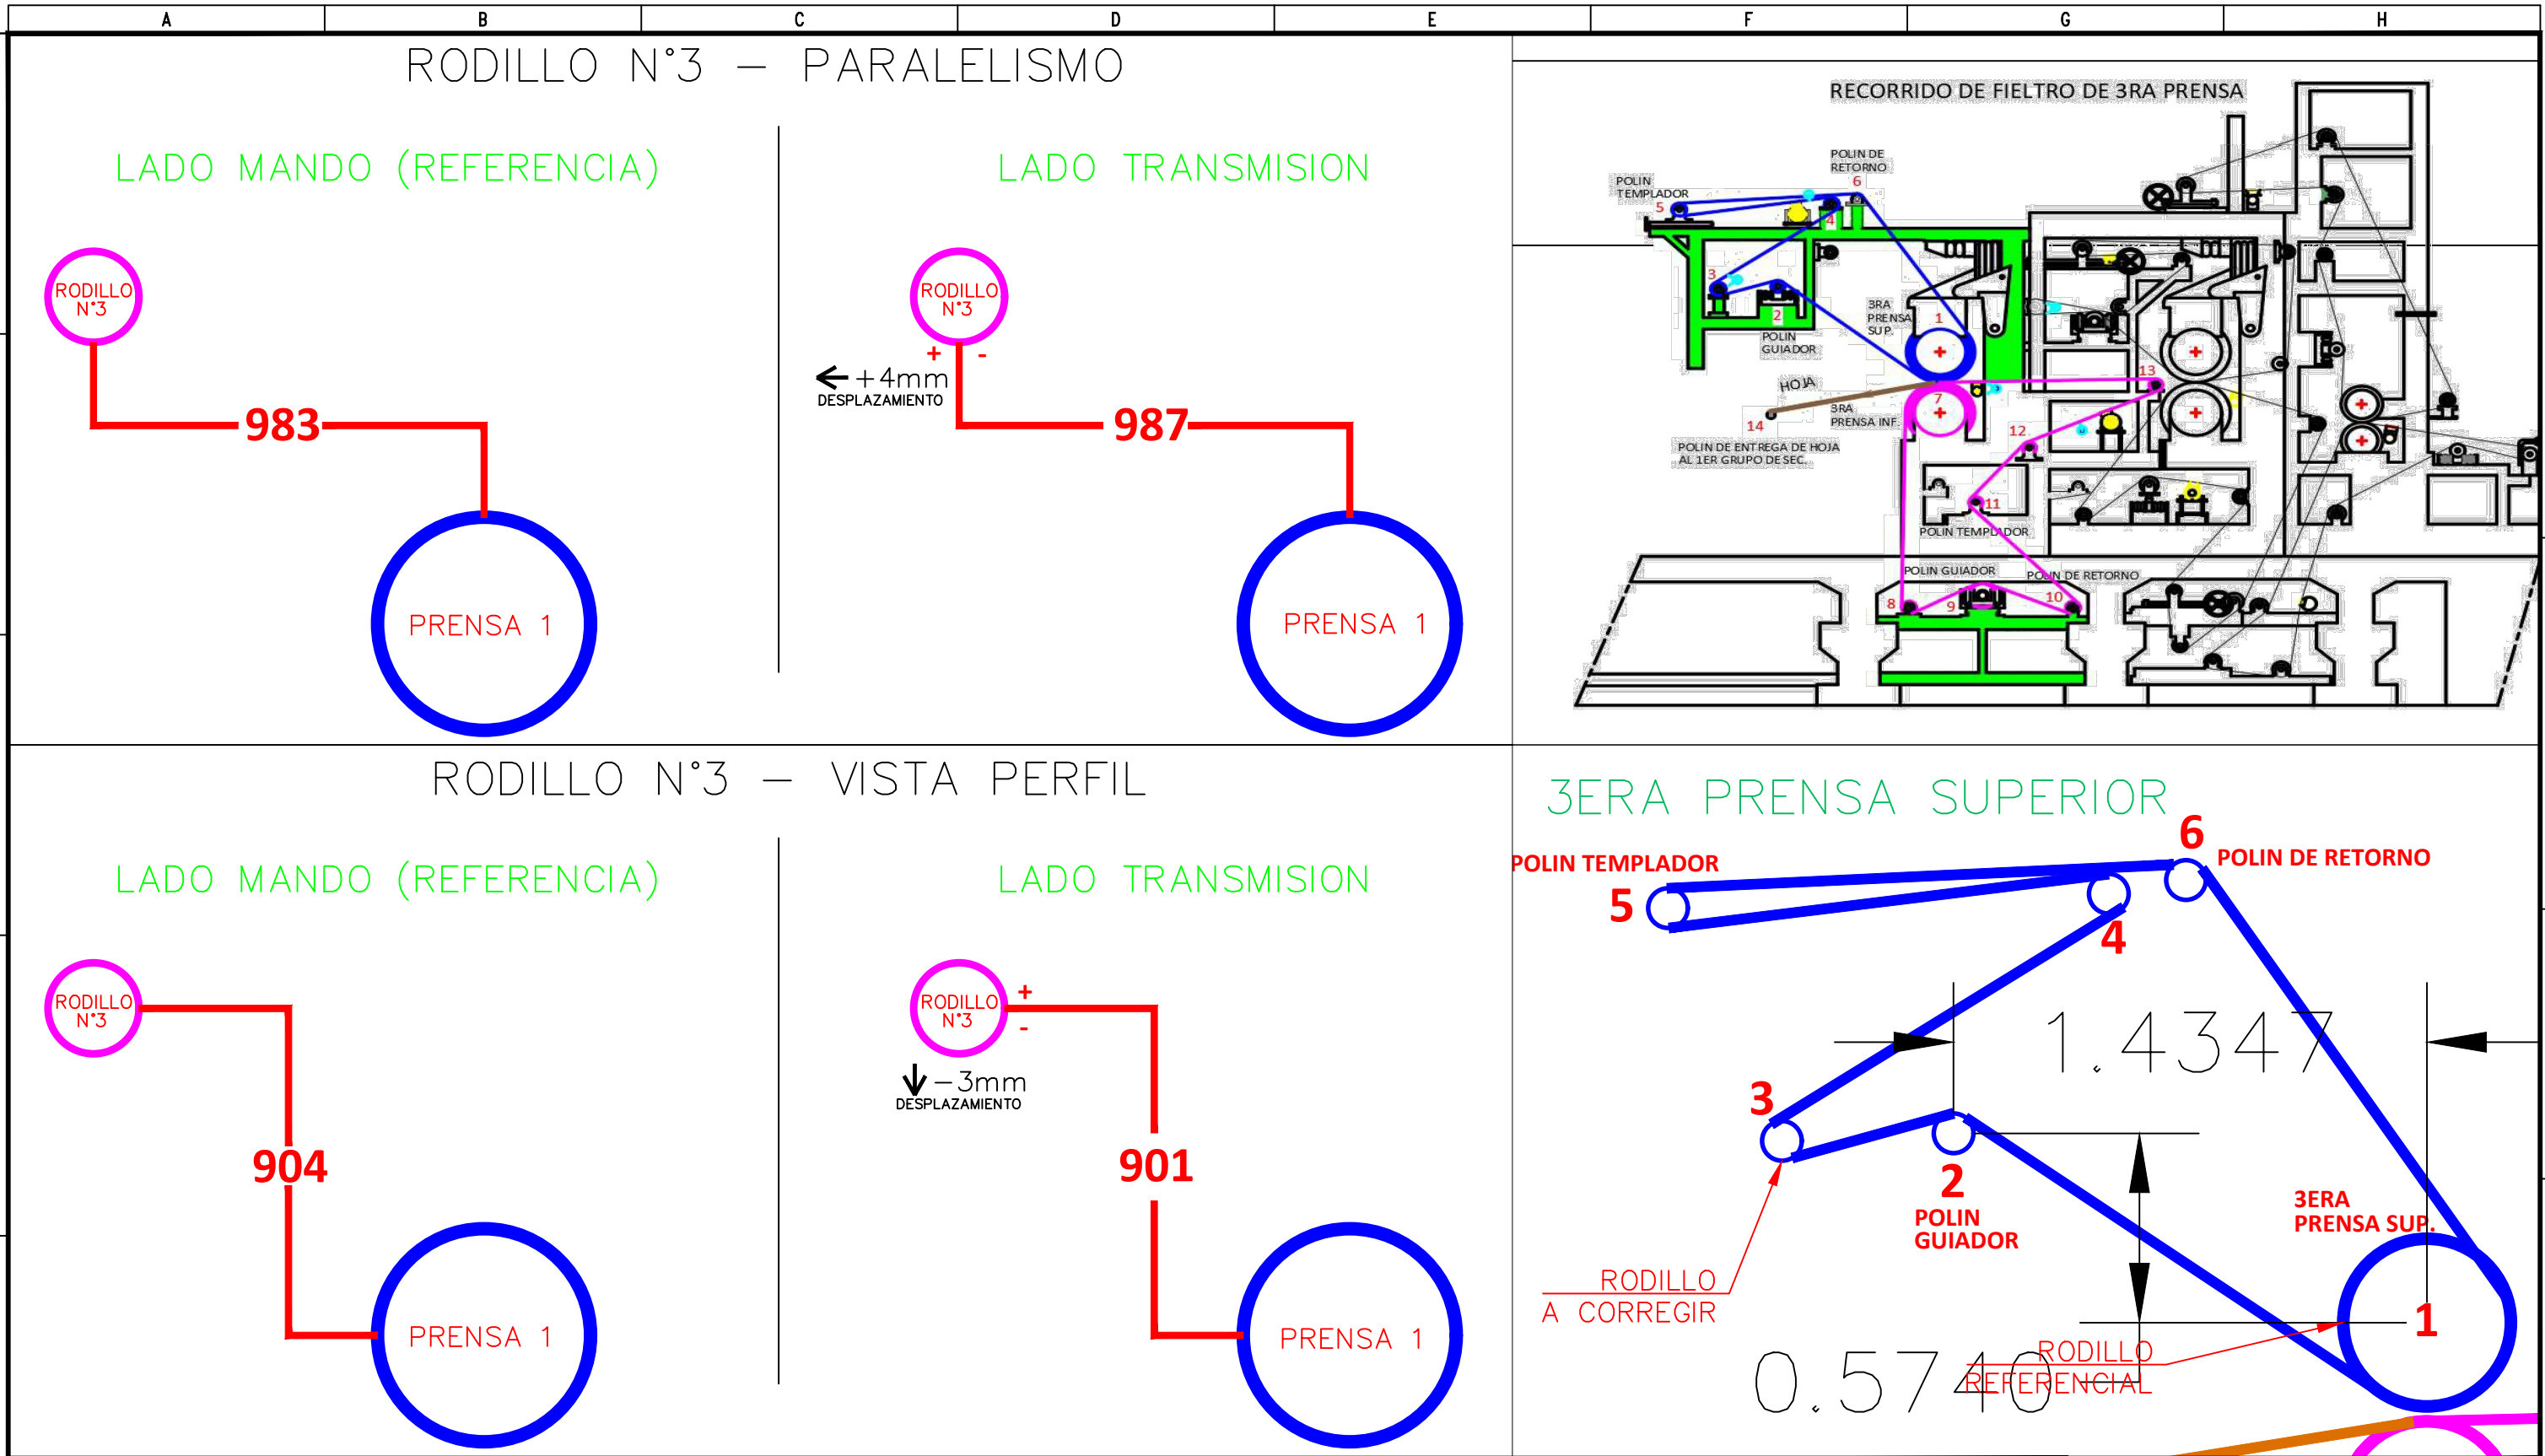

NOTA:

- LOS PUNTOS TOMADOS EN ESTE LEVANTAMIENTO HAN SIDO POR LADO TRANSMISION, CON REFERENCIA AL LADO MANDO, POR INDICACION DE EL CLIENTE.
- EN EL PRESENTE PLANO SE MUESTRA LA DESVIACION EN PARALELISMO Y NIVELACION DE LOS RODILLOS TANTO EN VISTA DE PERFIL COMO EN PLANTA.
- EL LEVANTAMIENTO SE REALIZO CON UNA ESTACION TOTAL LEICA TS09 PLUS.
- LAS DESVIACIONES MOSTRADAS TANTO EN NIVELACION COMO EN PARALELISMO ESTAN REFLEJADOS EN MILIMETROS A MENOS QUE SE INDIQUE LO CONTRARIO.
- LAS CORRECCIONES POSTERIORES AL PRESENTE INFORME, DEBEN REALIZARSE POR EL LADO TRANSMISION.

1A-MIG

PROYECTO: INDUSTRIA DEL PAPEL S.A. VERIFICACION Y ALINEAMIENTO CHACLACAYO – LURIGANCHO		
CONTENIDO: ALINEAMIENTO Y NIVELACION PRENSA SUPERIOR 3 – RODILLO N°3		
N° PLANO CLIENTE: 1AMIG-TOP-109	LAMINA N° A3	REV. A